



1st Floor FloorID: 6515_01

Printed On: 2/20/2021

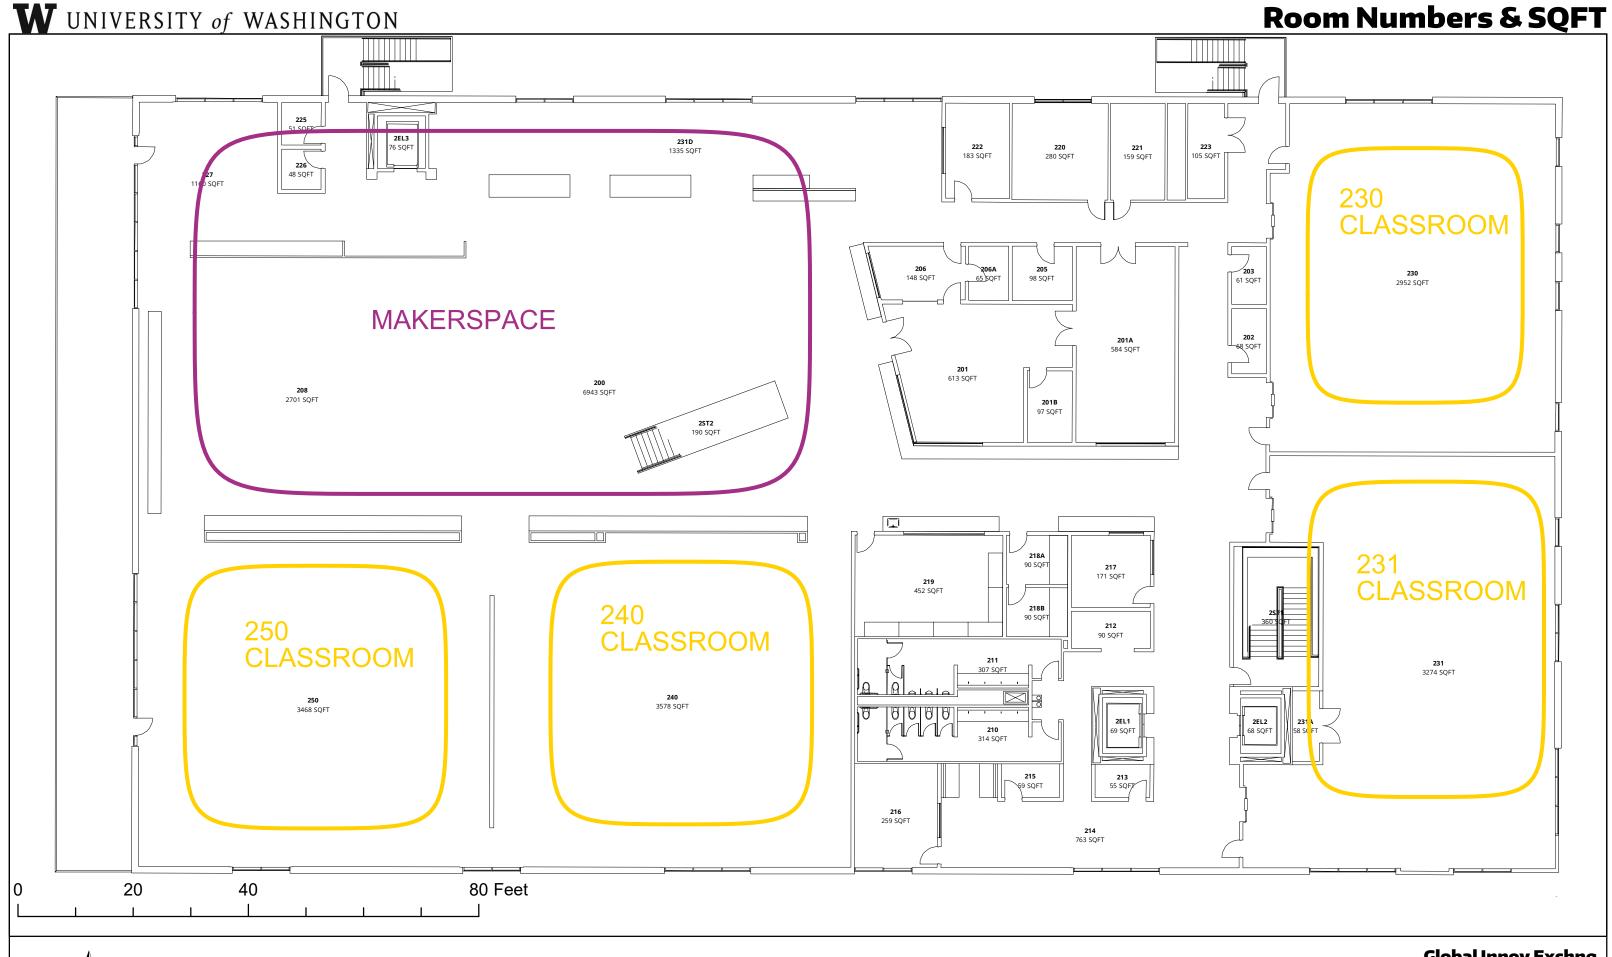

Global Innov Exchng 2nd Floor FloorID: 6515_02 Printed On: 2/20/2021

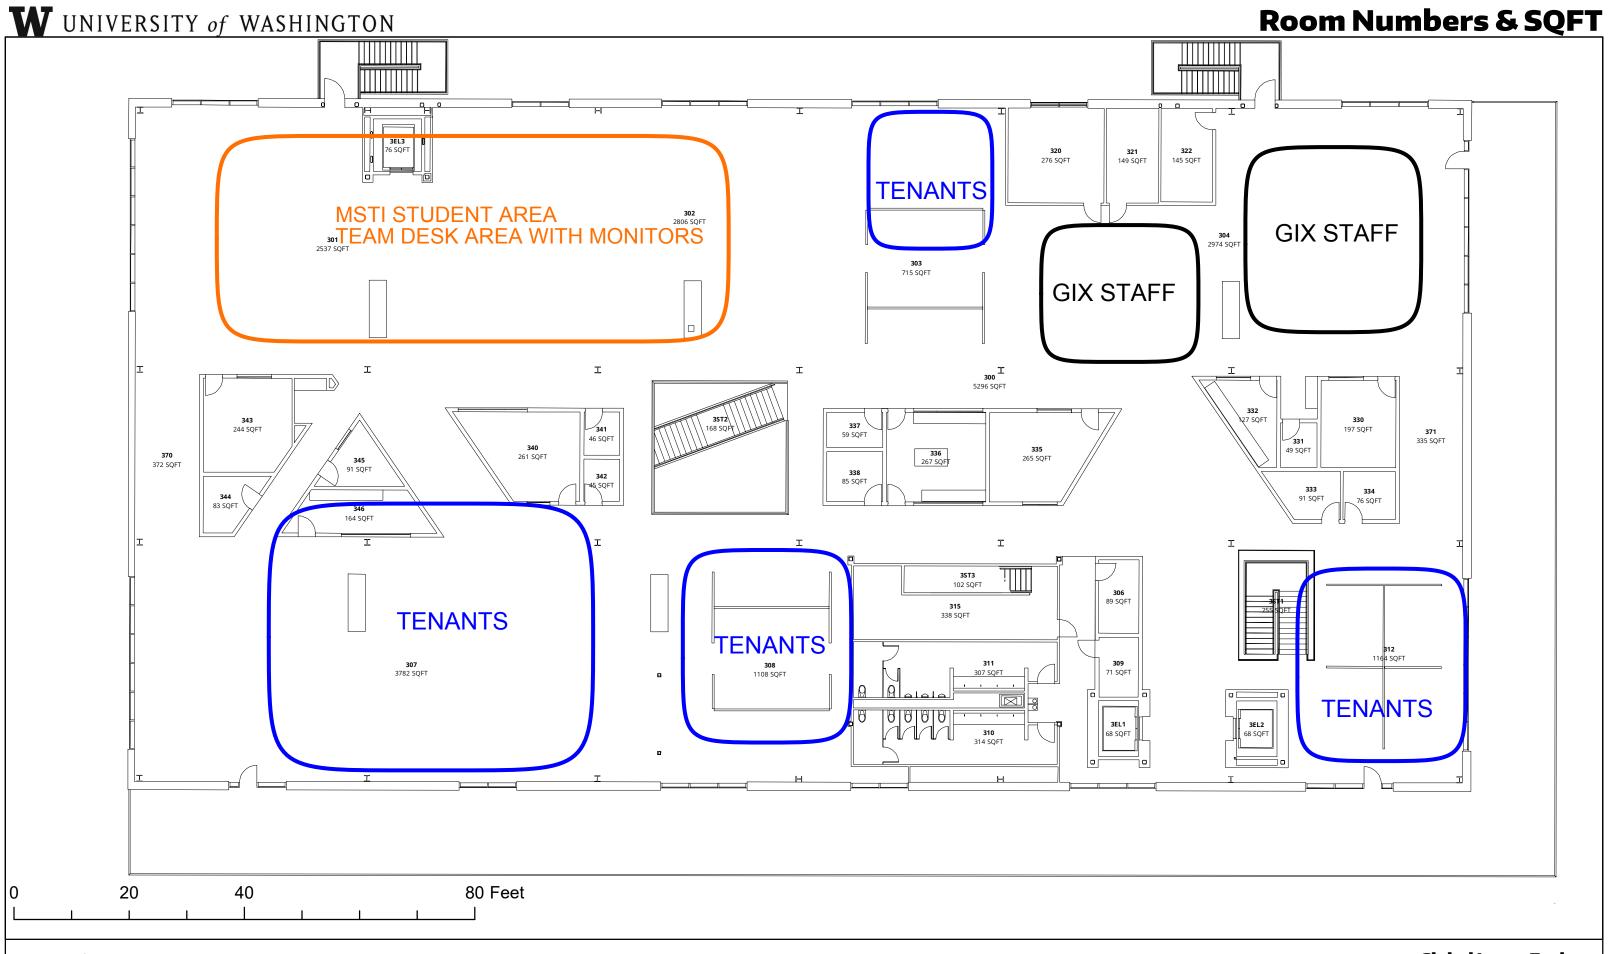

Global Innov Exchng 3rd Floor FloorID: 6515_03 Printed On: 2/20/2021